


ИНДИВИДУАЛЬНЫЙ ЖИЛОЙ ДОМ

Регион строительства: Ленинградская область

ПРОЕКТНАЯ ДОКУМЕНТАЦИЯ

Эскизный проект

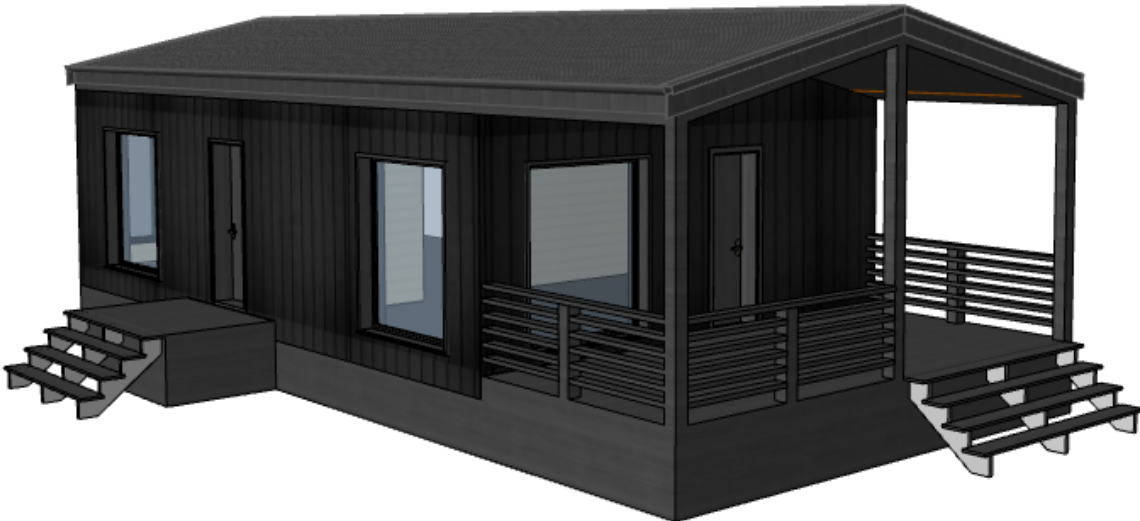

Ведомость чертежей


Лист	Наименование	Примечание
1	План 1-го этажа	
2	План кровли	
3	Разрез 1-1	
4	Разрез 2-2	
5	Фасад в осях 1-5	
7	Фасад в осях 5-1	
8	Фасад в осях Г-А	
9	Общий вид 1	
9	Фасад в осях А-Г	
10	Общий вид 2	
11	Ведомость заполнения проемов	

Технико-экономические показатели


Этажность здания	1 этаж
Высота 1-го этажа, м	3,2
Минимальная высота 1-го этажа	2,5
Площадь застройки, м²	84,06
Общая площадь помещений, м²	50,86
Общая площадь (помещений, террас и т.п.), м²	72,69


Ведомость помещений 1-го этажа

№ п/п	Наименование	Площадь
1.1	Спальня	9,10
1.2	Спальня	9,10
1.3	С/У	3,04
1.4	Тамбур	8,74
1.5	Кухня-гостиная	20,87
1.6	Терраса	18,50
1.7	Крыльцо	3,33
		72,69 м²

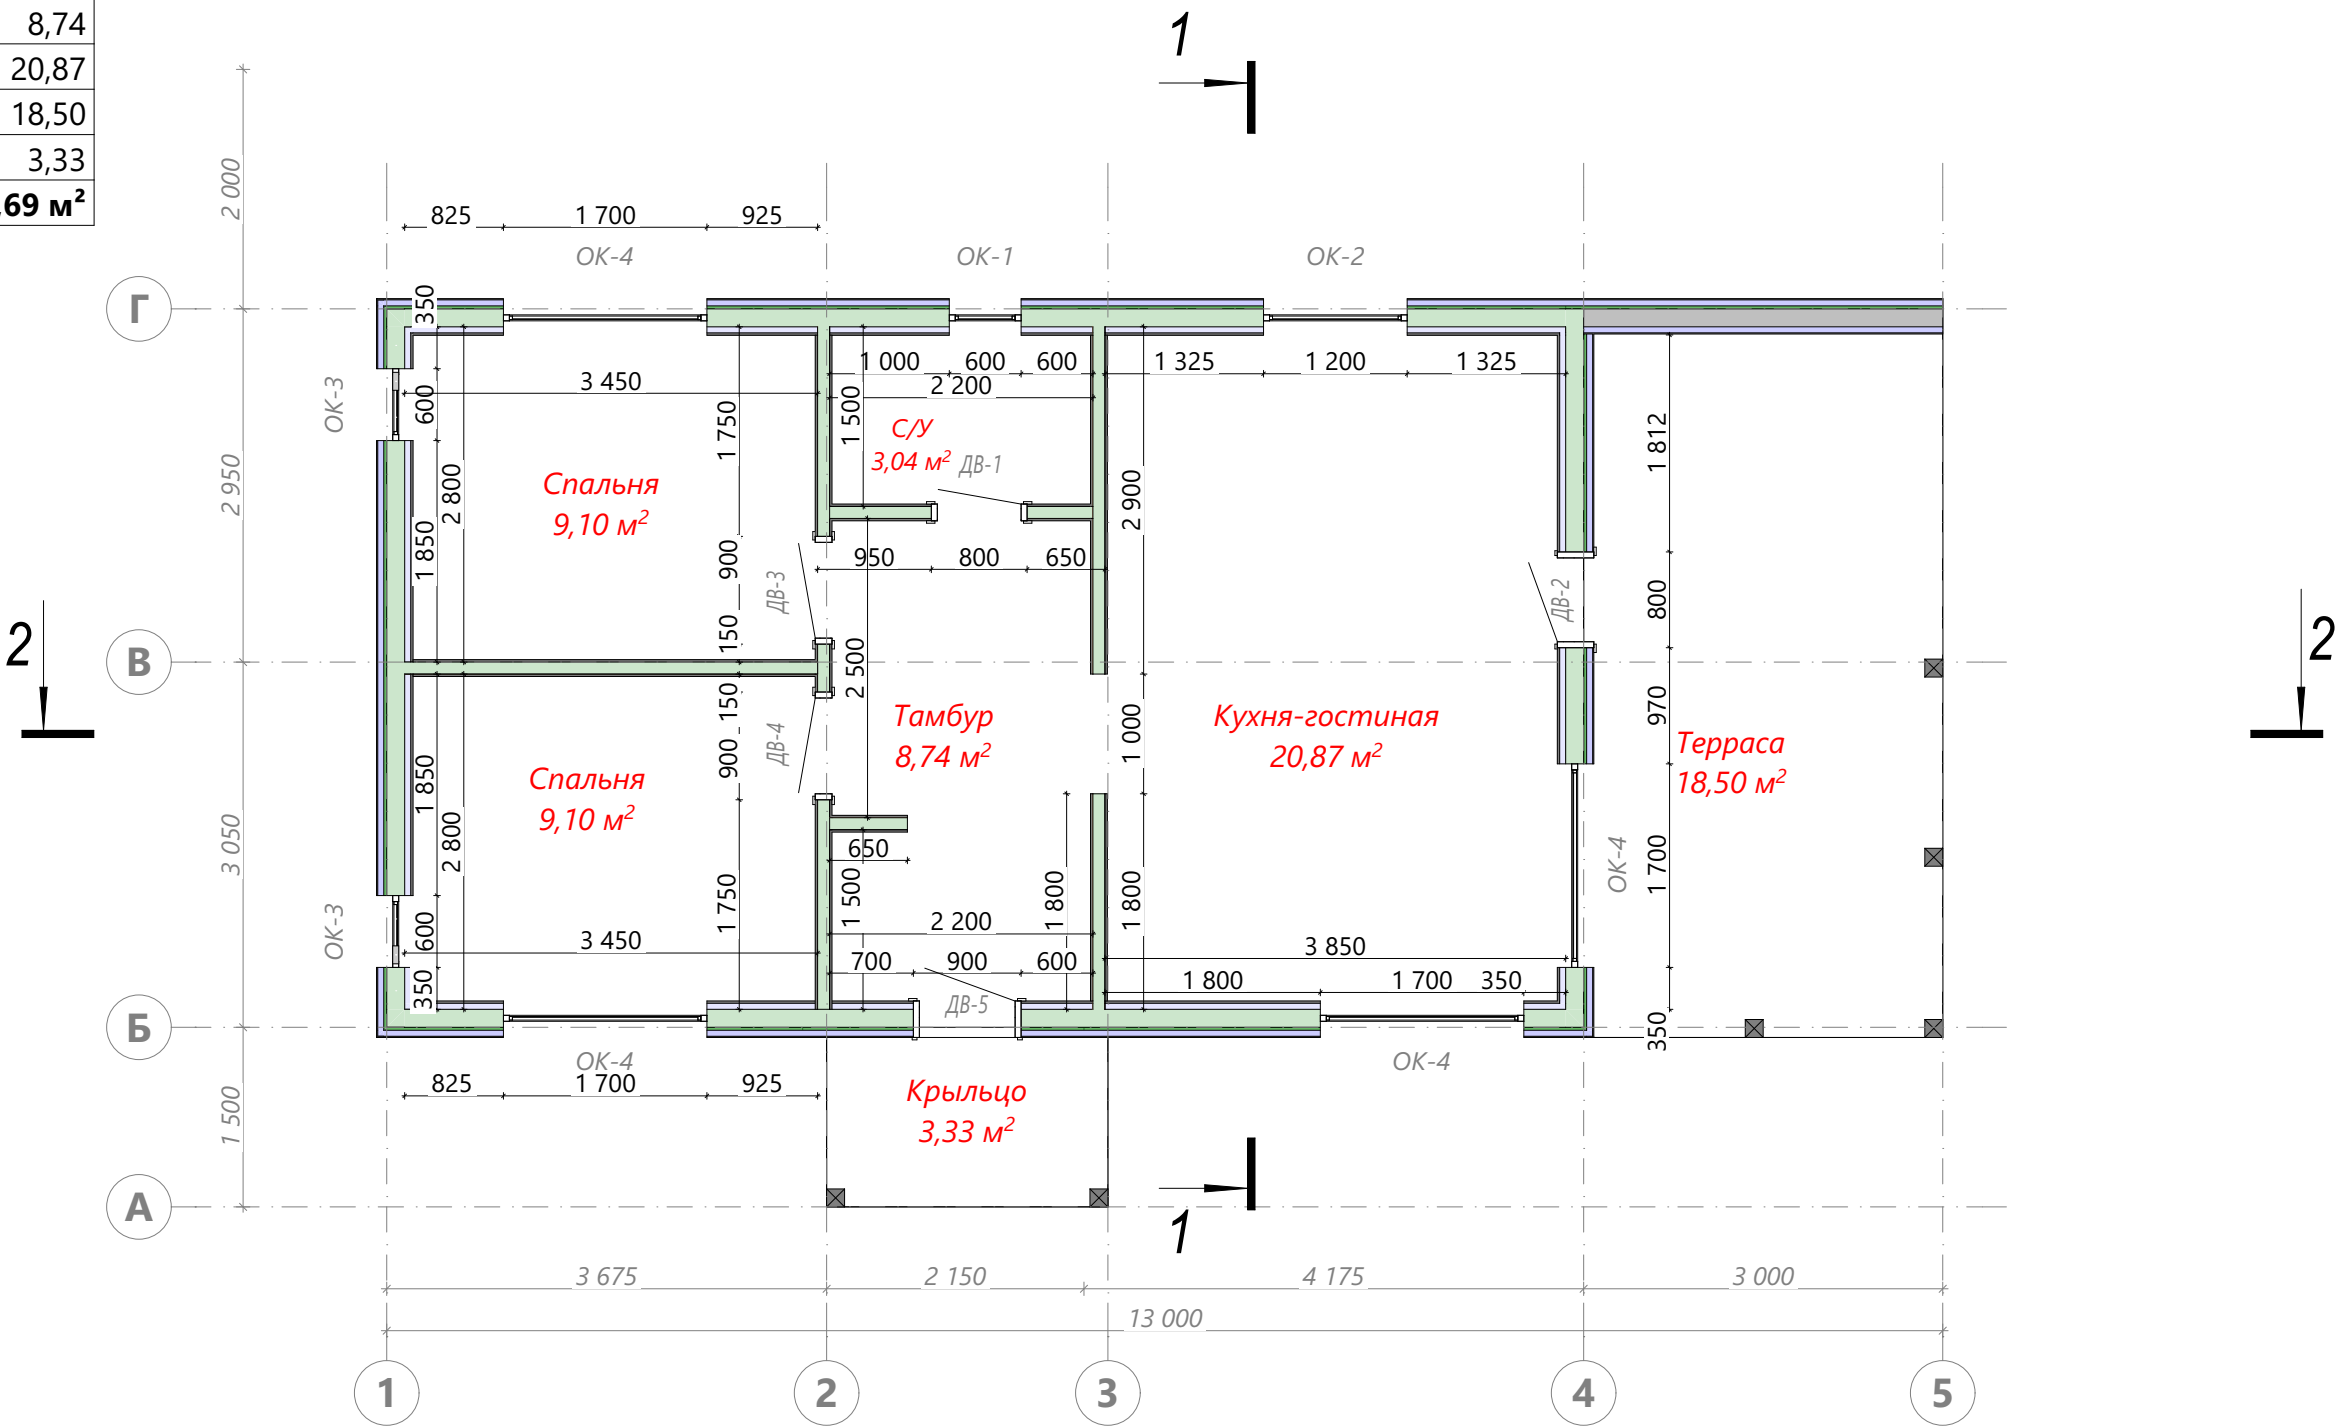

Примечание:
1. В качестве размера дверного проема указана ширина дверного полотна.
2. В качестве размера оконного проема указана ширина оконного блока.
3. Размеры отображены по каркасу

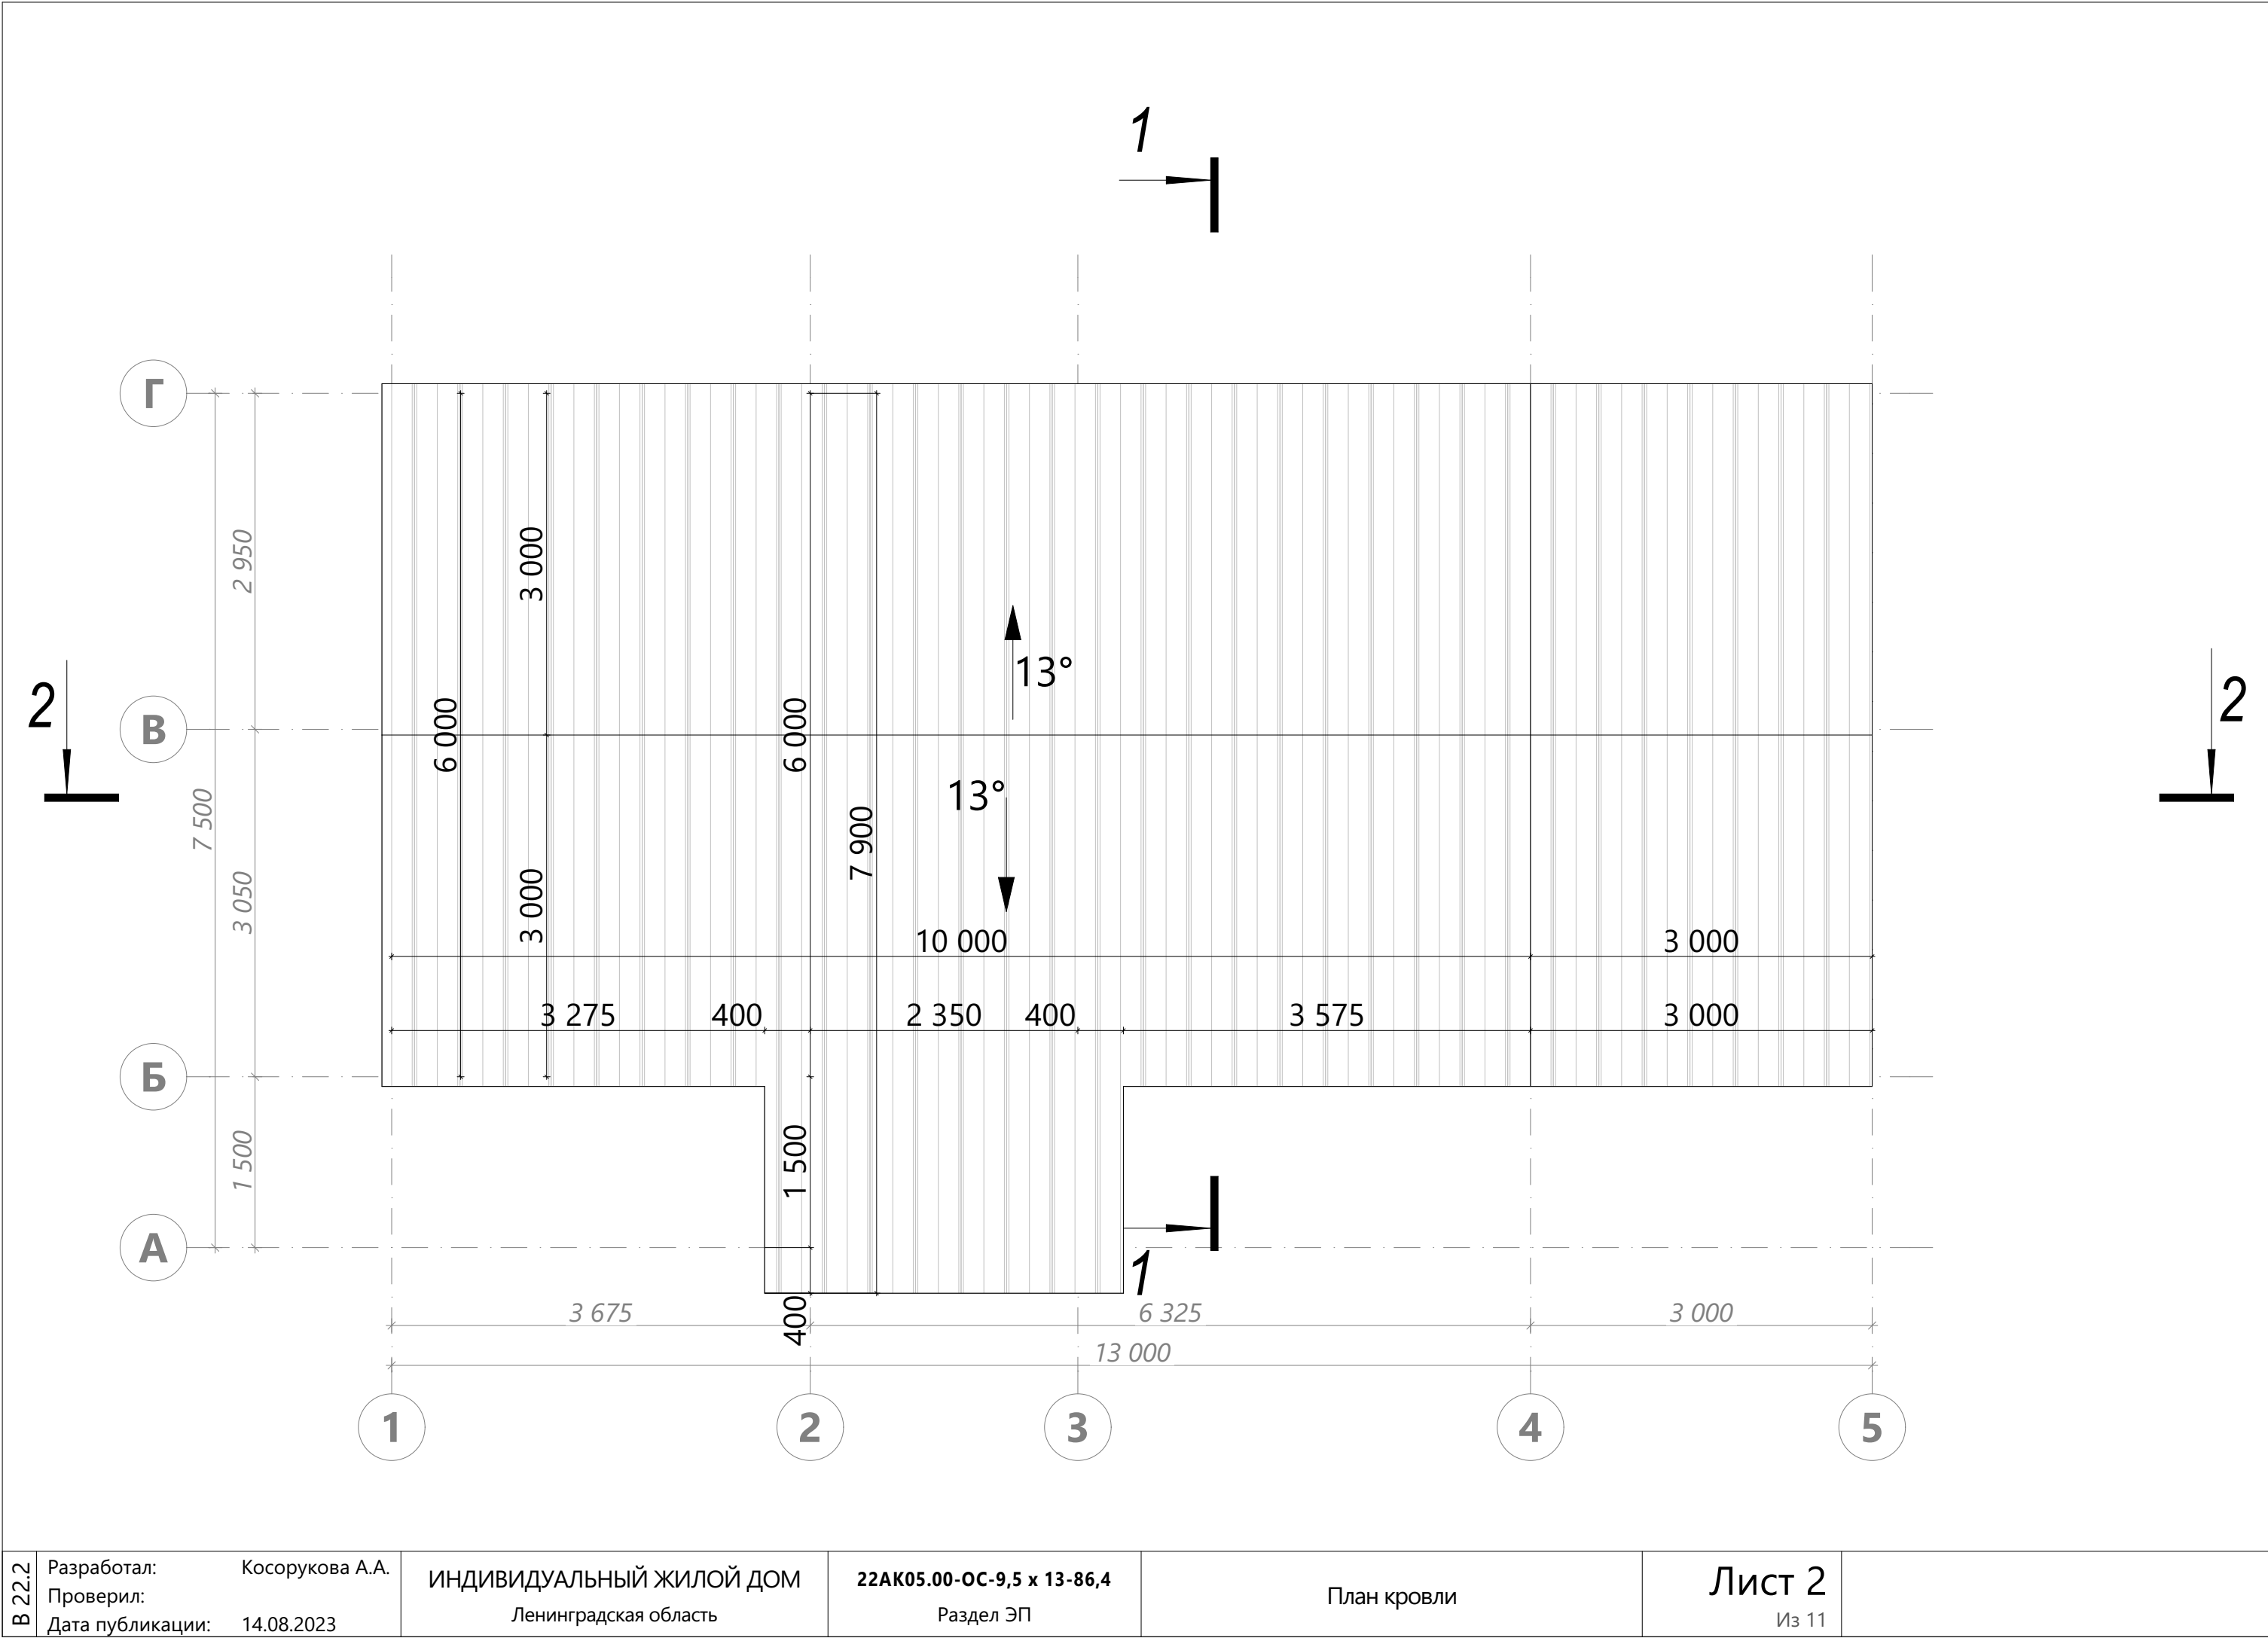


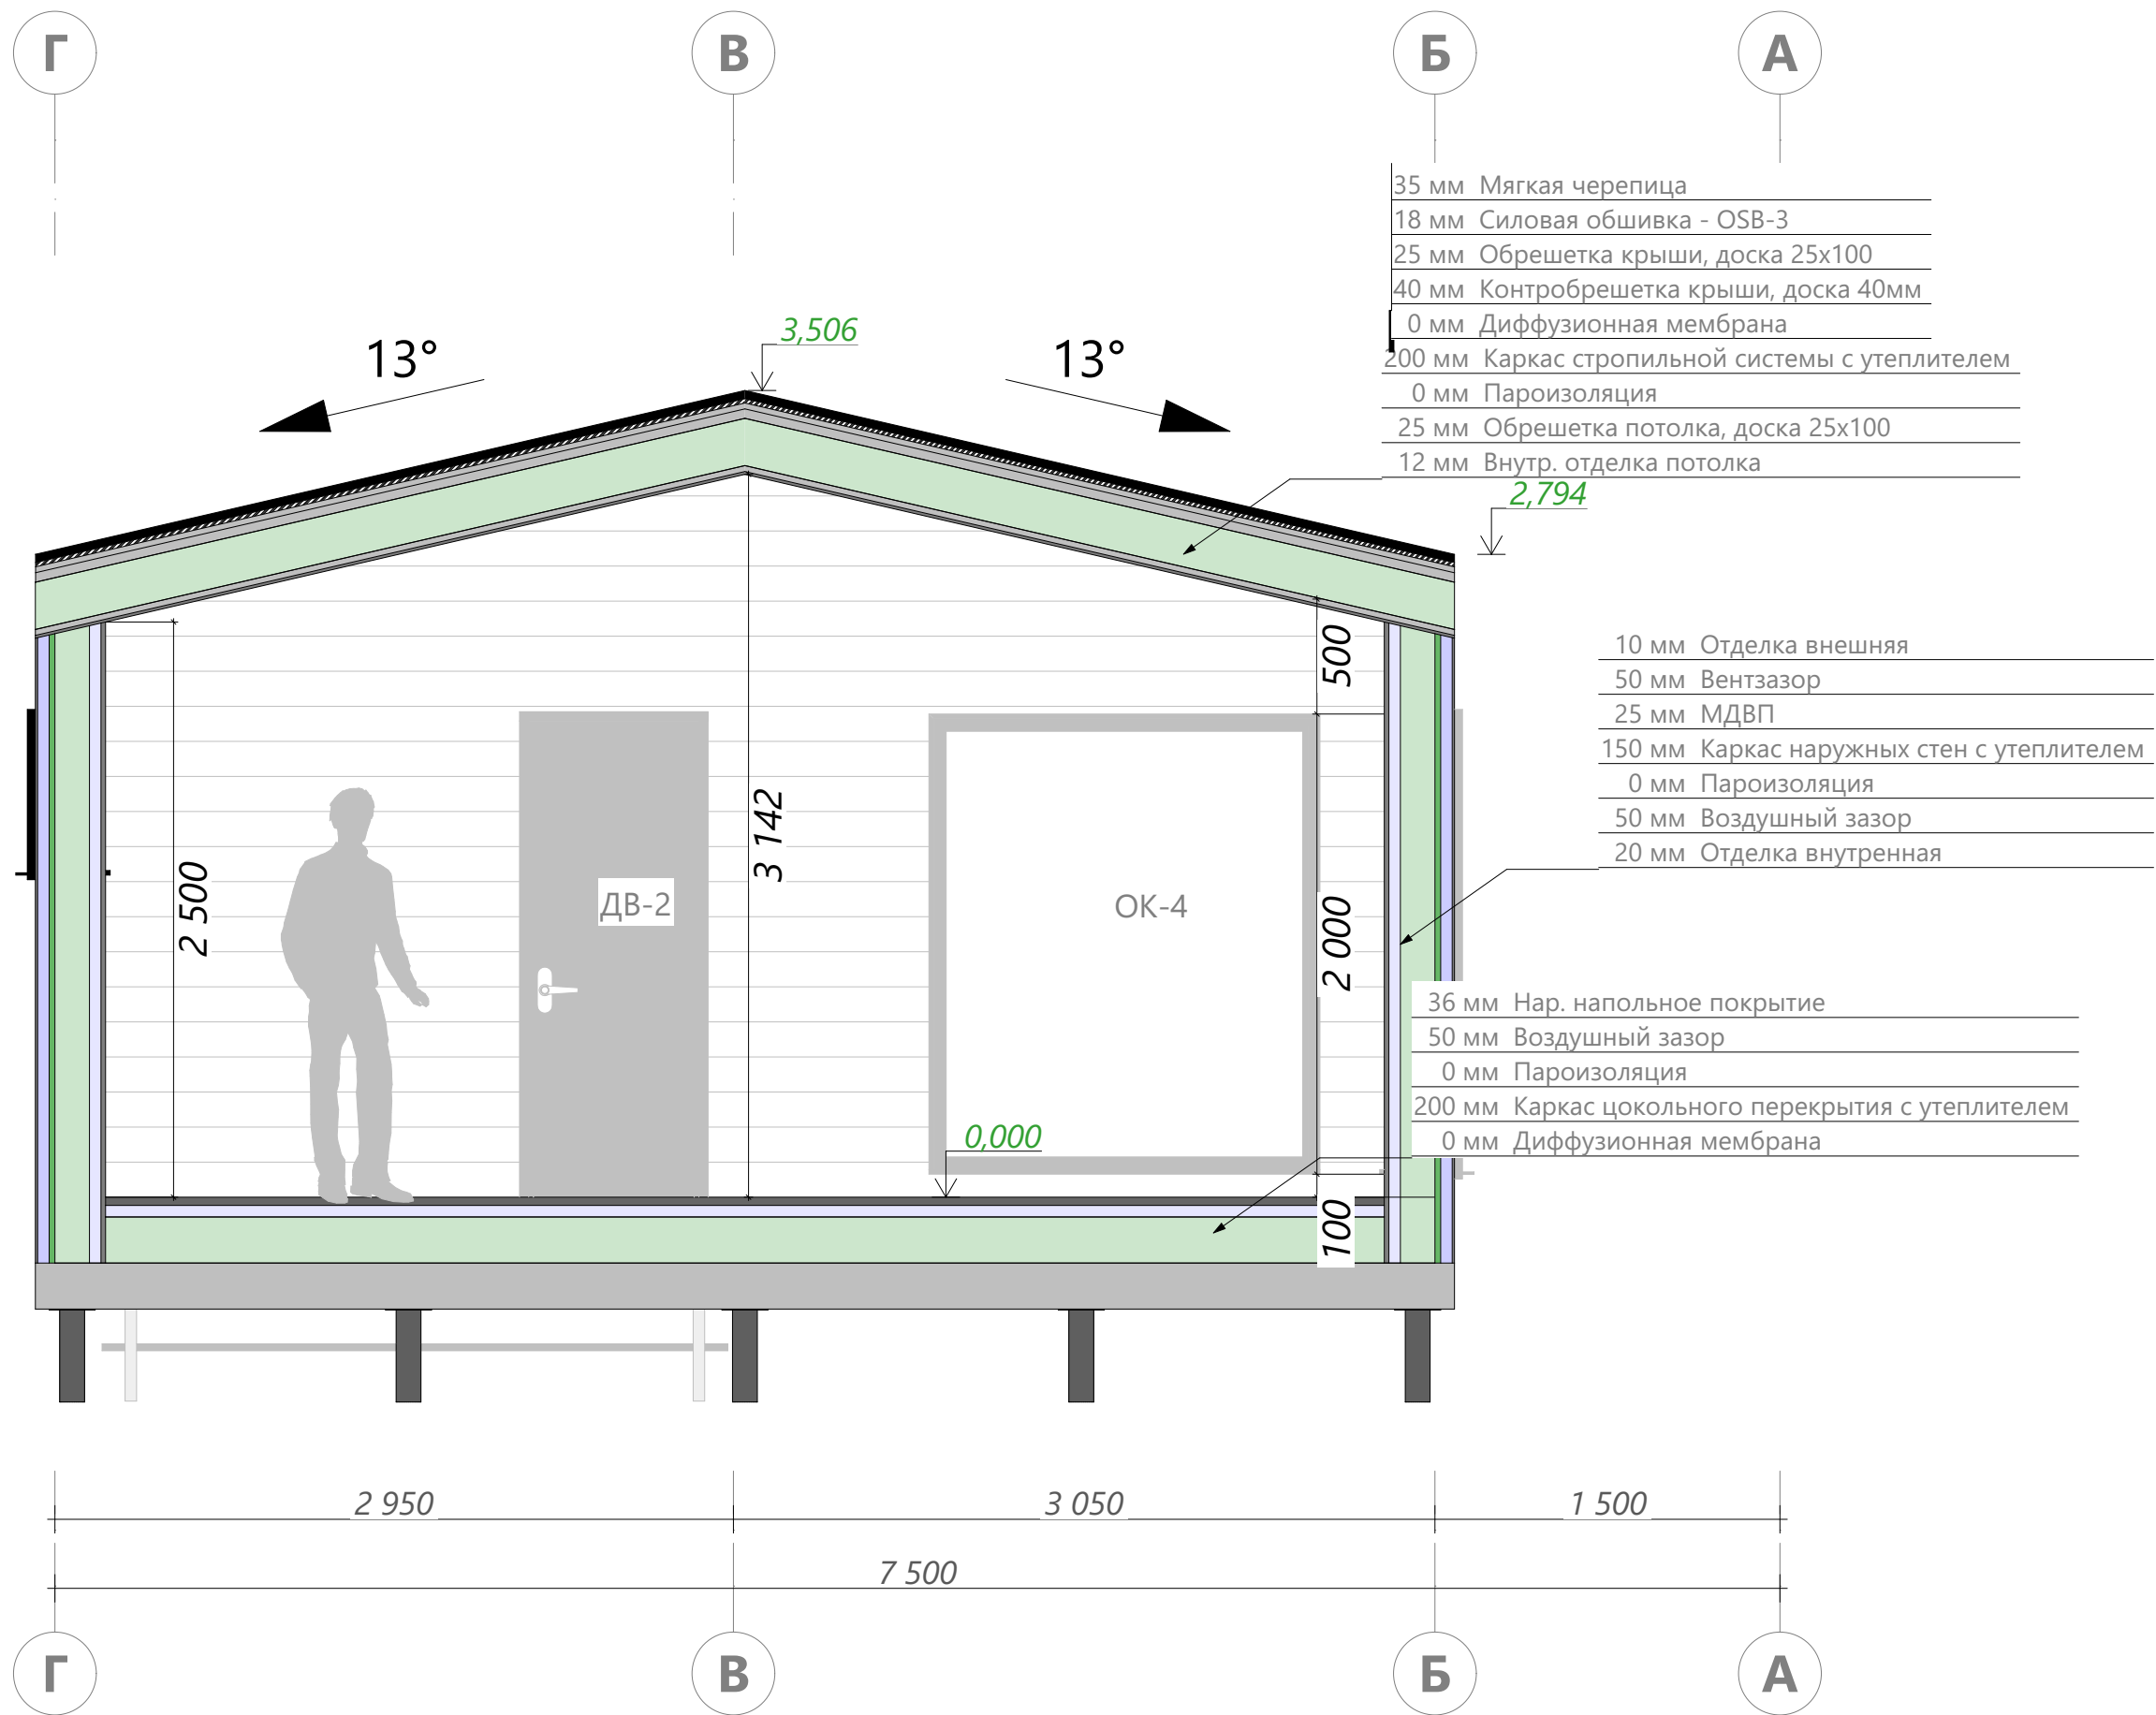

Примечание:

1. В качестве высоты дверного проема указана высота дверного полотна.
2. За уровень 0,000 принят уровень чистового покрытия пола 1-го этажа.
3. Высота фигуры человека 1800 мм.
4. Размеры указаны по отделке


В 22.2	Разработал:	Косорукова А.А.	ИНДИВИДУАЛЬНЫЙ ЖИЛОЙ ДОМ Ленинградская область	22АК05.00-ОС-9,5 x 13-86,4 Раздел ЭП	Разрез 1-1	Лист 3 Из 11
	Проверил:					
	Дата публикации:	14.08.2023				

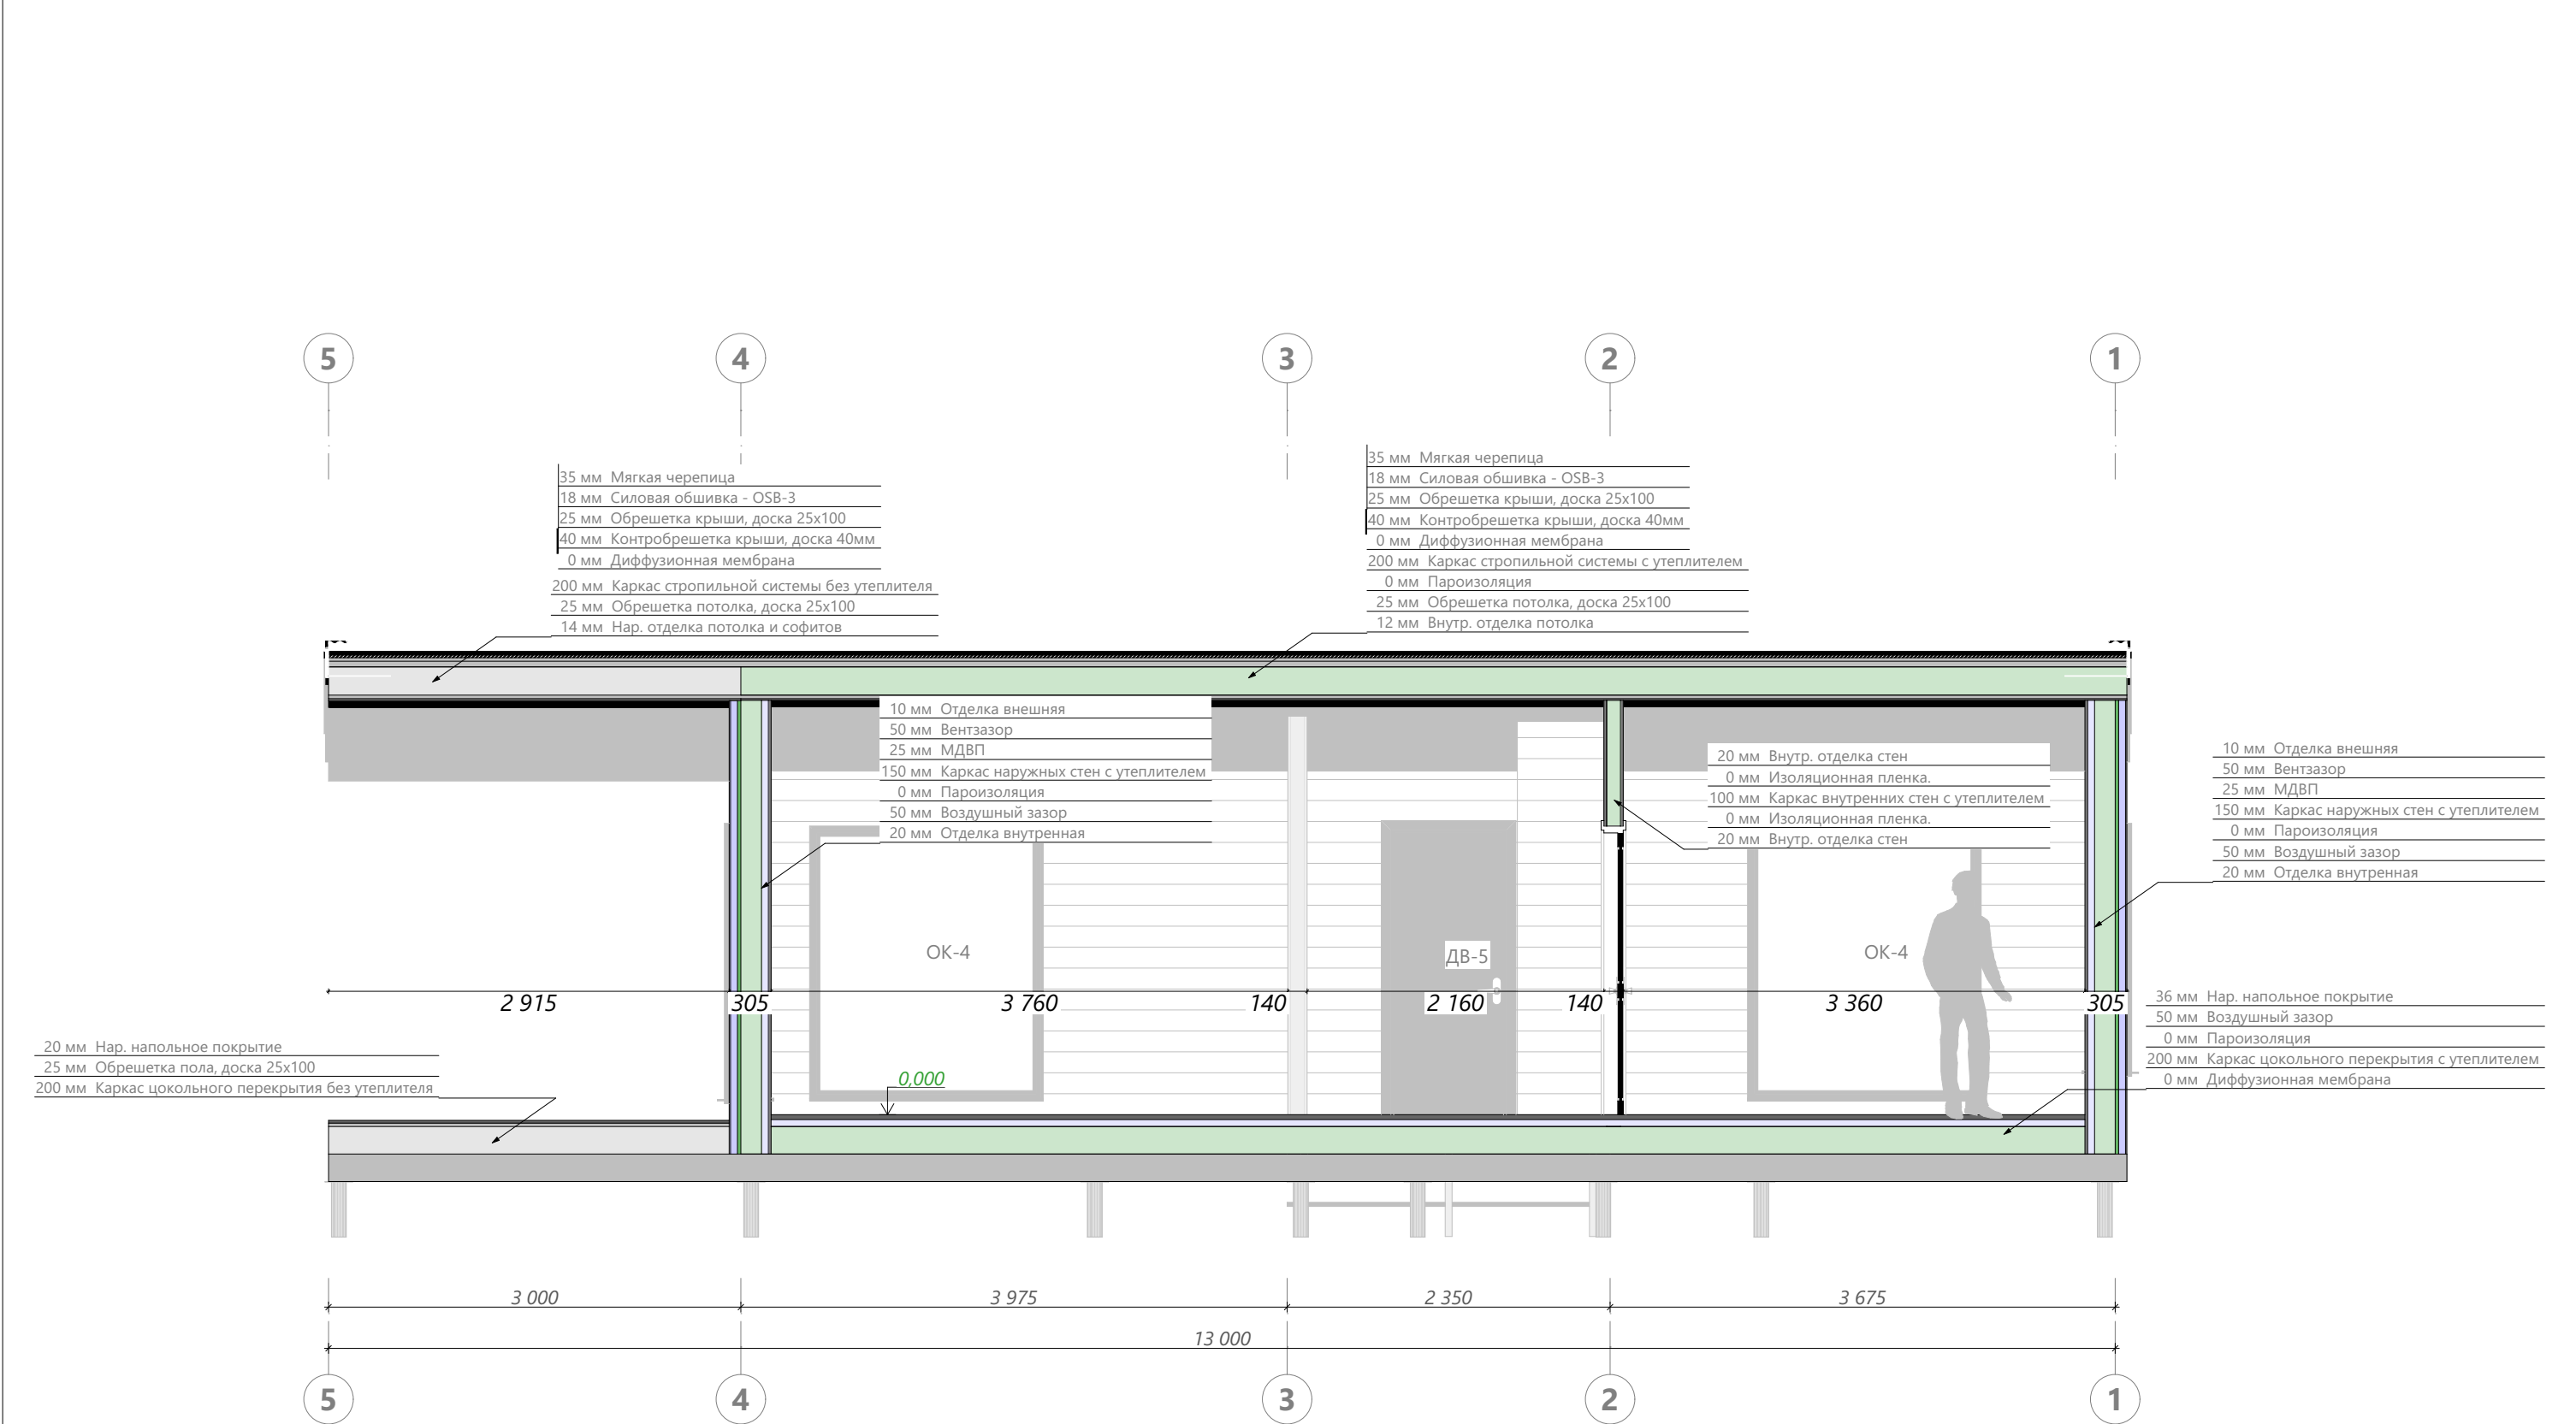



Примечание:


1. В качестве высоты дверного проема указана высота дверного полотна.
2. За уровень 0,000 принят уровень чистового покрытия пола 1-го этажа.
3. Высота фигуры человека 1800 мм.
4. Размеры указаны по отделке.

В 22.2	Разработал: Косорукова А.А. Проверил: Дата публикации: 14.08.2023	ИНДИВИДУАЛЬНЫЙ ЖИЛОЙ ДОМ Ленинградская область	22АК05.00-ОС-9,5 x 13-86,4 Раздел ЭП	Разрез 2-2	Лист 4 Из 11
--------	---	---	---	------------	-----------------

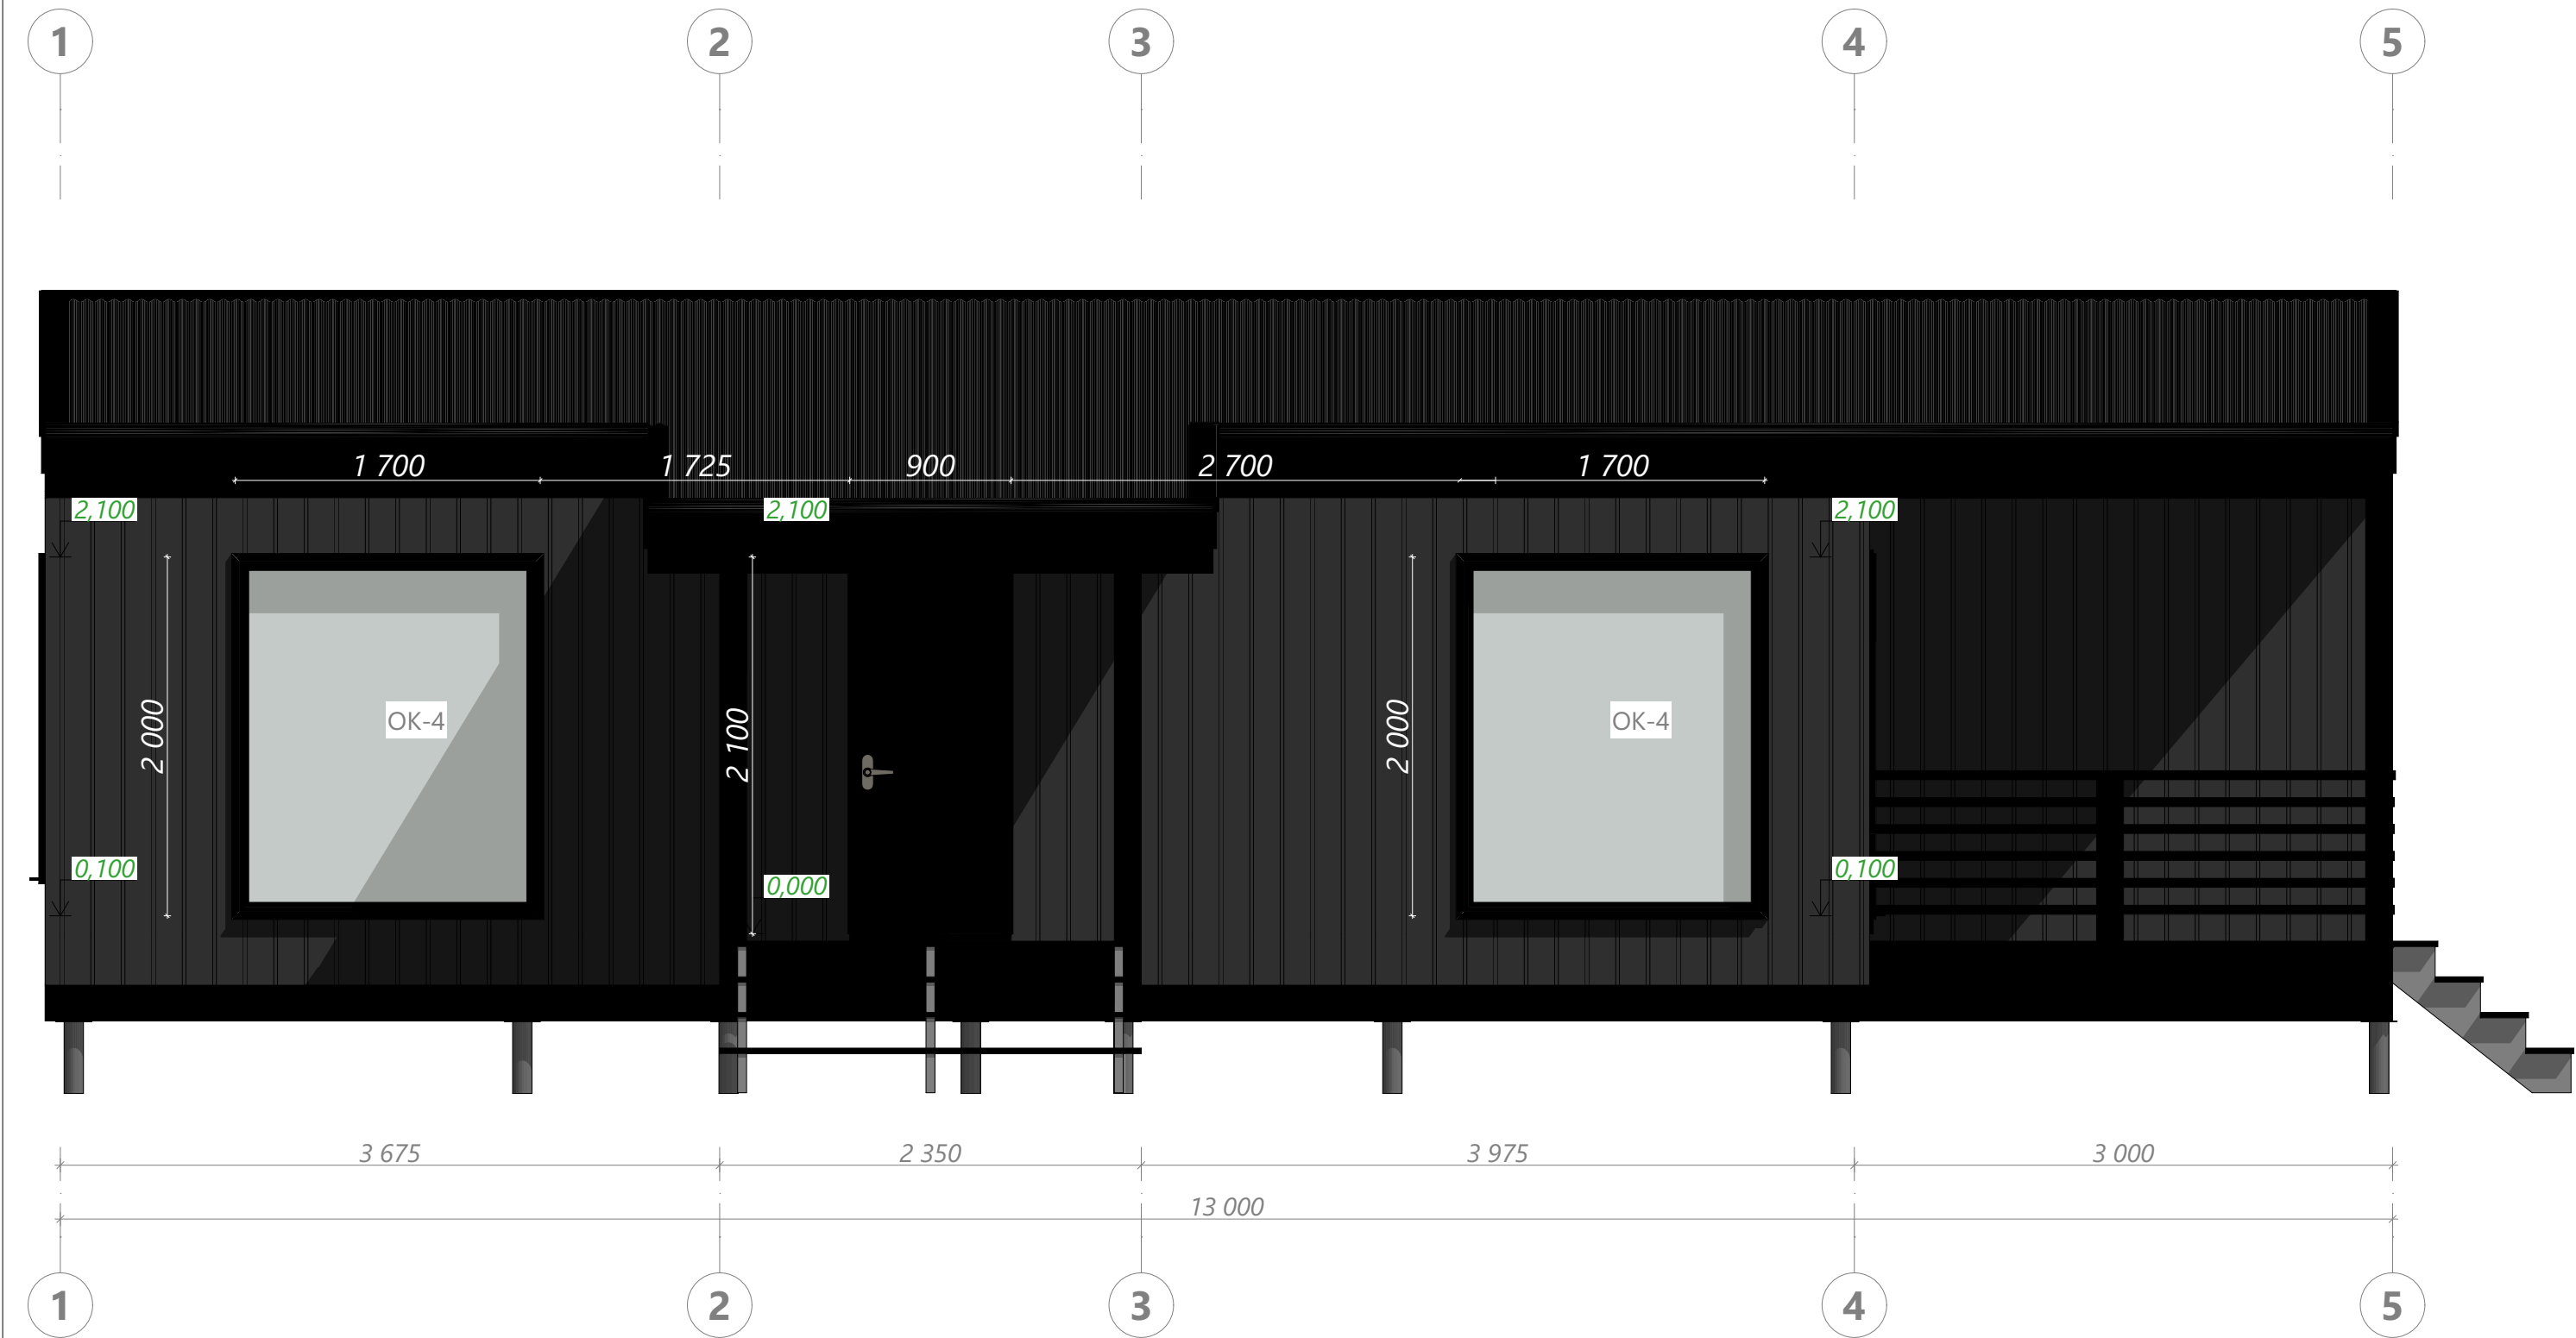

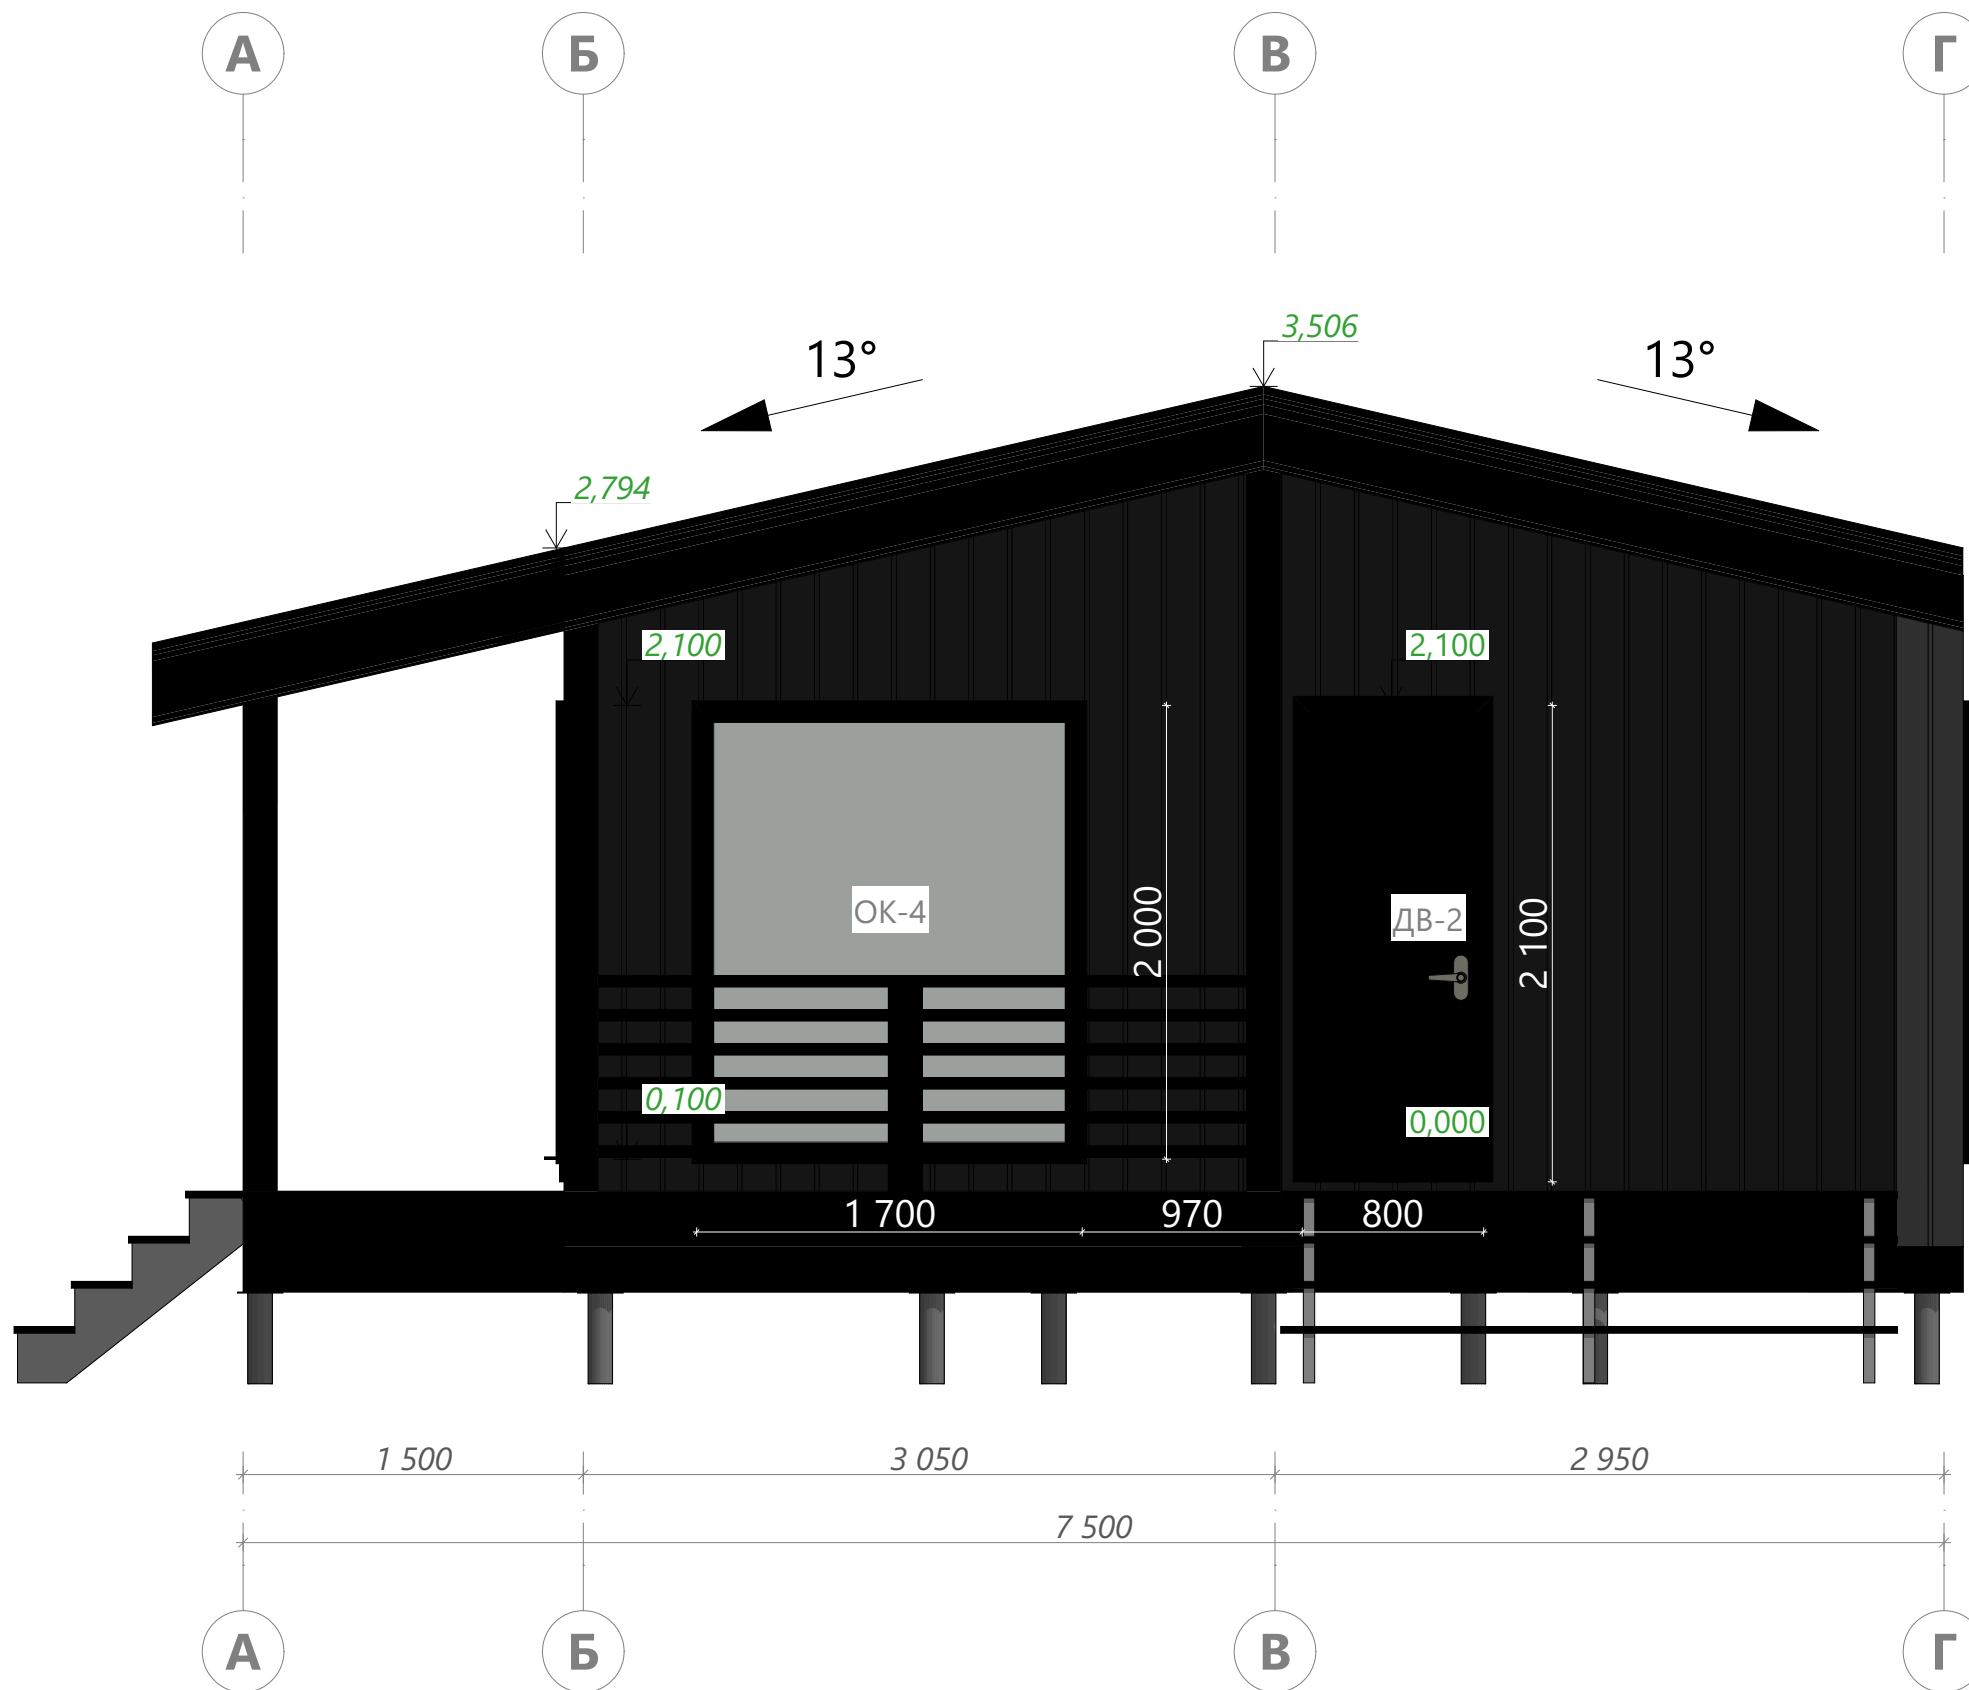

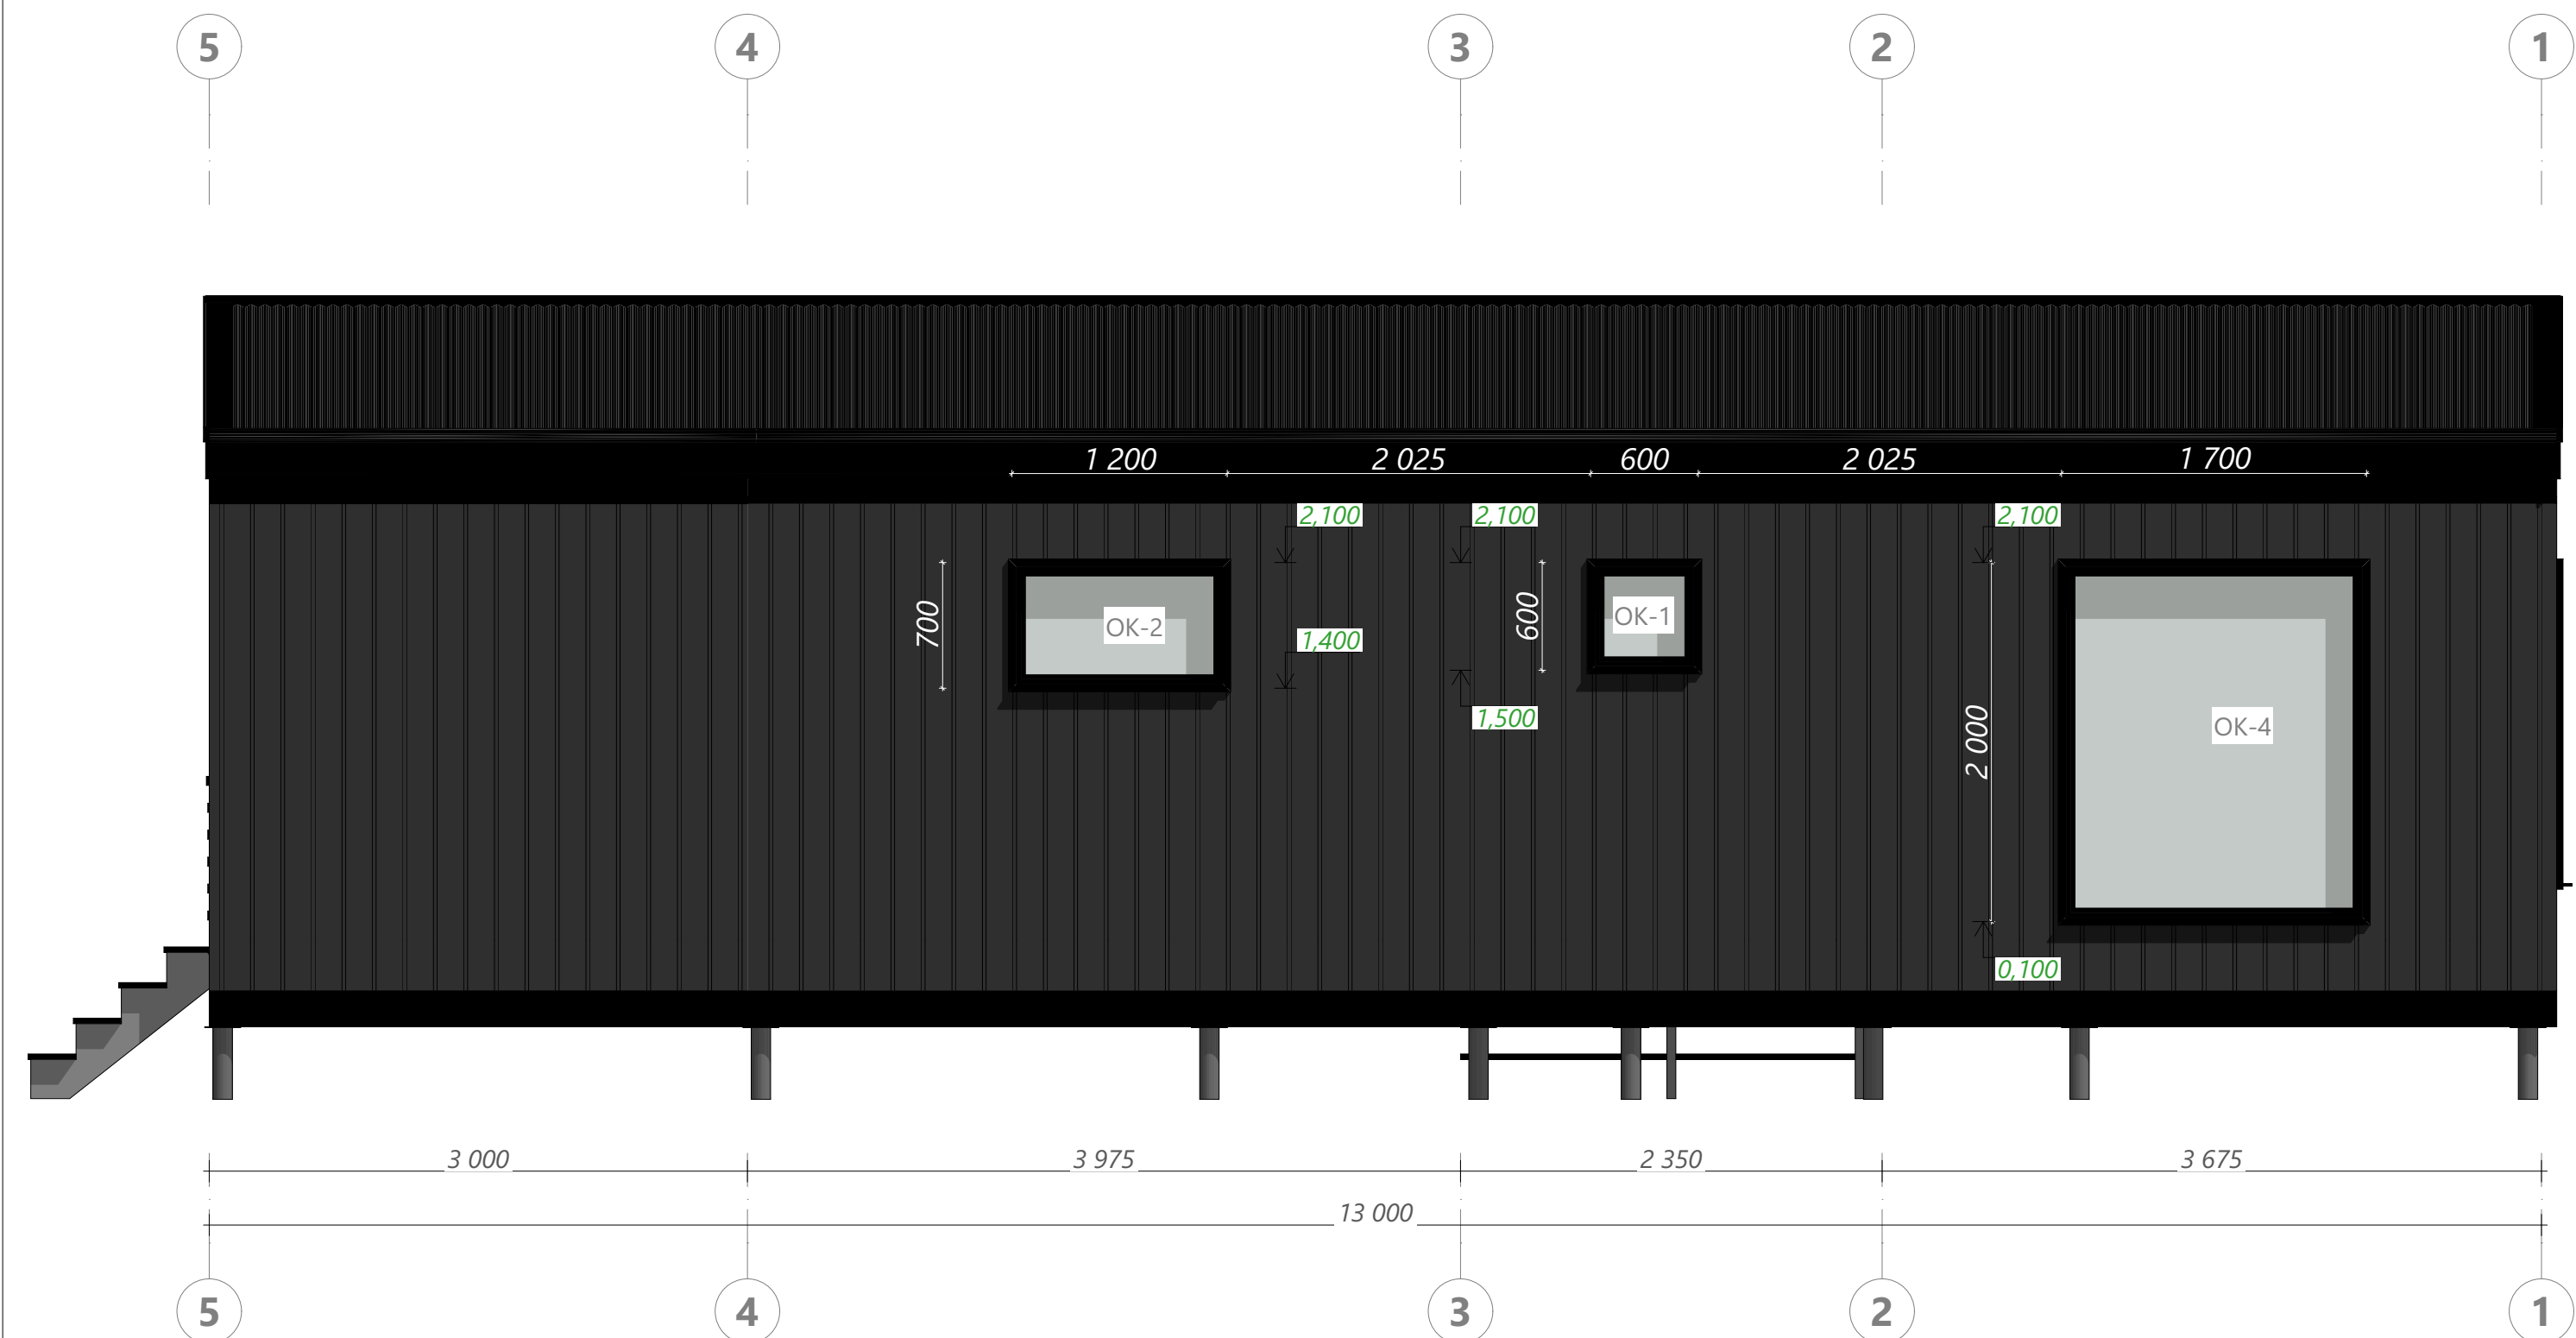


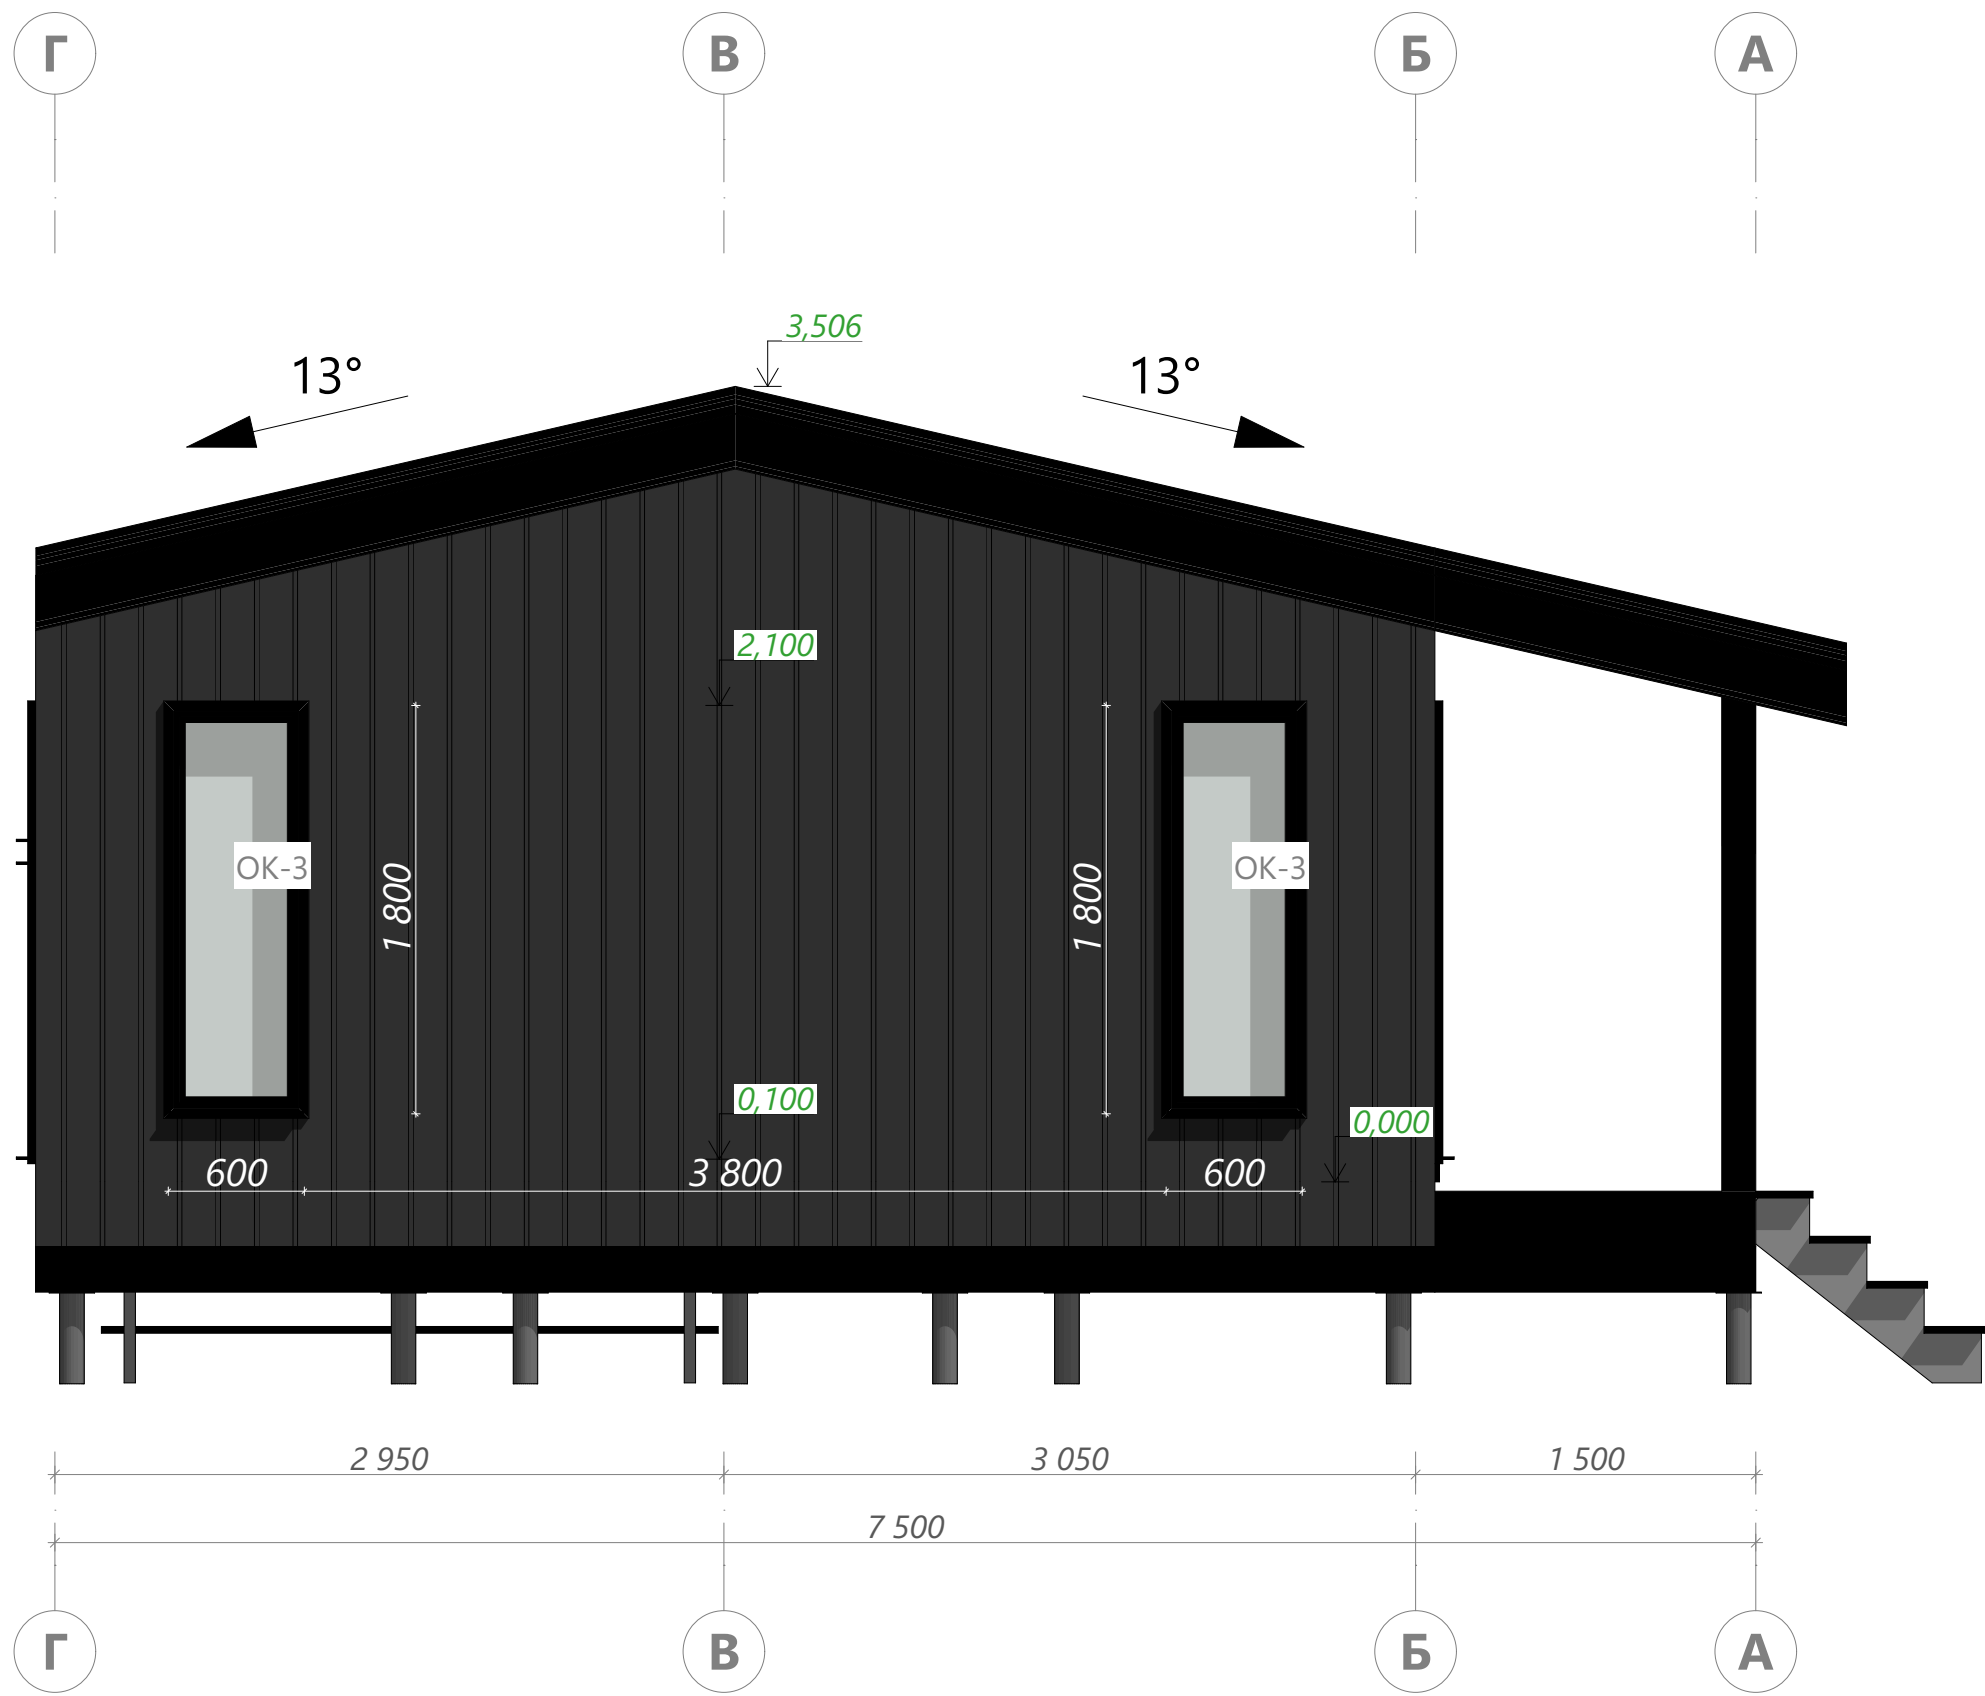








Ведомость заполнения оконных проемов

 Поз.	Вид с наружной стороны здания	Размеры оконного блока (Ш x В)	Кол-во	Площадь оконного блока
ОК-1		600×600	1	0,36
ОК-2		1 200×700	1	0,84
ОК-3		600×1 800	2	1,08
ОК-4		1 700×2 000	4	3,40

8 16,96 м²

Ведомость заполнения дверных проемов

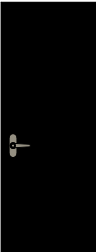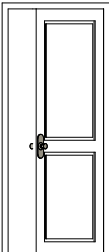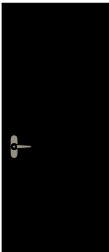Поз.	Вид спереди	Размеры полотна (Ш x В)	Ори-ция	Кол-во	Площадь Проема
ДВ-1		700×2 050	Л	1	1,68
ДВ-2		700×2 050	П	1	1,68
ДВ-3		800×2 050	П	1	1,89
ДВ-4		800×2 050	Л	1	1,89
ДВ-5		800×2 050	Л	1	1,89

5 9,03 м²

Примечание:
1. Размеры оконных блоков указаны без учета подставочного профиля